

DNS_1

dns1 - 192.168.240.2
dhcp - 192.168.240.2
intra - 192.168.240.2
partage - 192.168.240.6
controleur - 192.168.240.6
dns2 - 192.168.240.6
imprimante1 - 10.0.1.65
domotique1 - 10.0.4.1
television1 - 10.0.5.1
client1 - 10.0.2.1
telephone1 - 10.0.6.1
telephone2 - 10.0.6.2

DNS_2

dns1 - 192.168.240.2
dhcp - 192.168.240.2
intra - 192.168.240.2
partage - 192.168.240.6
controleur - 192.168.240.6
dns2 - 192.168.240.6
direction1 - 10.0.1.1
client2 - 10.0.2.2


Client n°1 : Hôtel Svart

Entreprise : EcoNet Normandie

RENAULT Louison; DELAFOSSE Quentin



Groupe : 1C2

Poste 4 (1er étage)

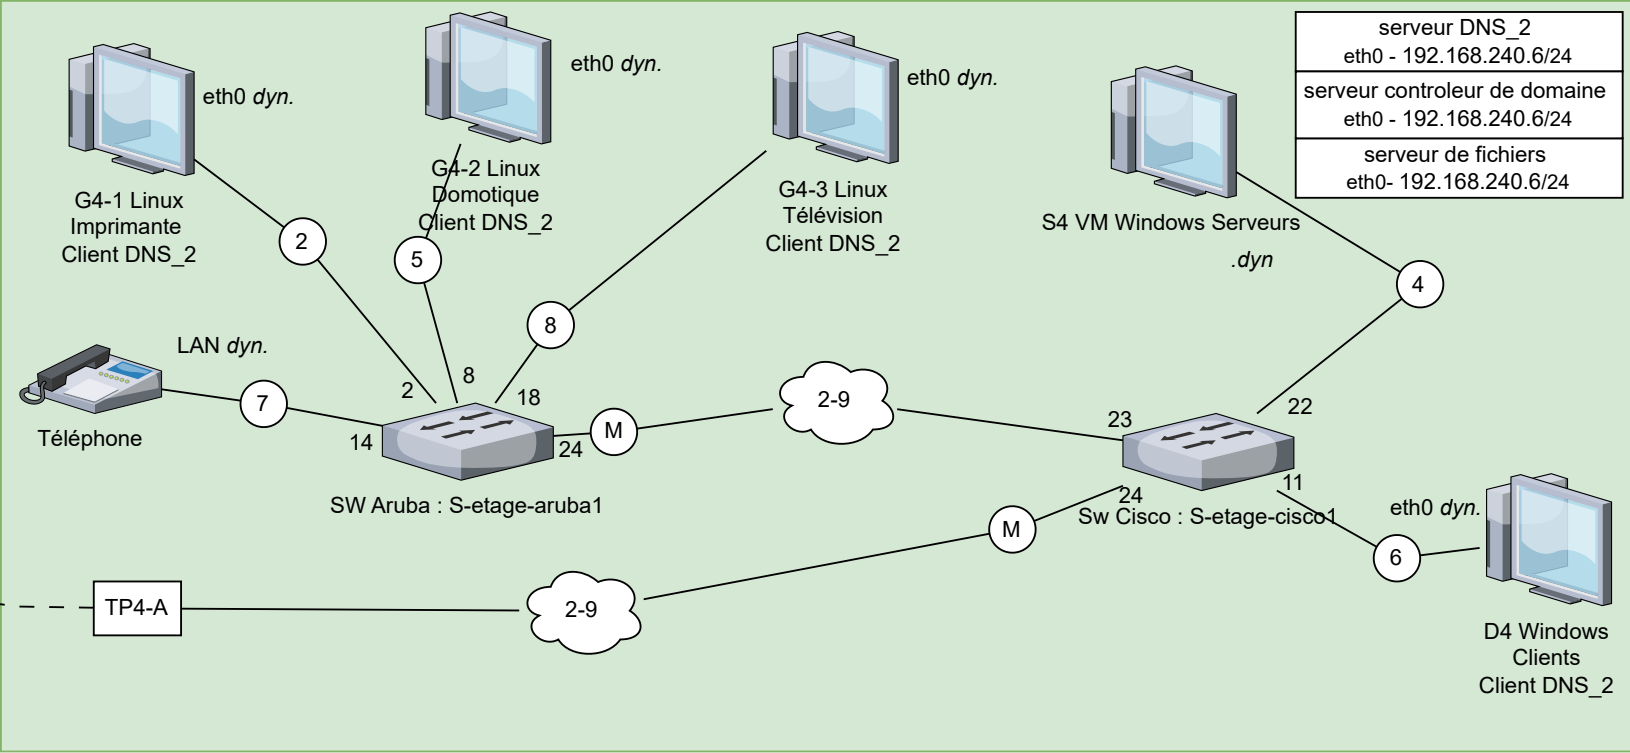


Vlan		
Num VLAN	Nom	Adresse IPV4
2	Imprimantes	10.0.1.64/29
3	Employés	10.0.0.0/24
4	Serveurs	192.168.240.0/24
5	Domotiques	10.0.4.0/24
6	Clients	10.0.2.0/23
7	Téléphones	10.0.6.0/24
8	Télévisions	10.0.5.0/24
9	Direction	10.0.1.0/26

Baie de brassage

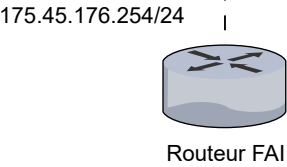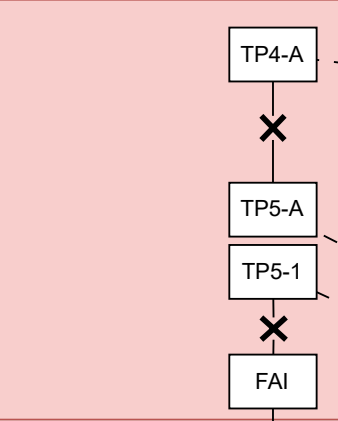

Poste 5 (rez de chaussée)

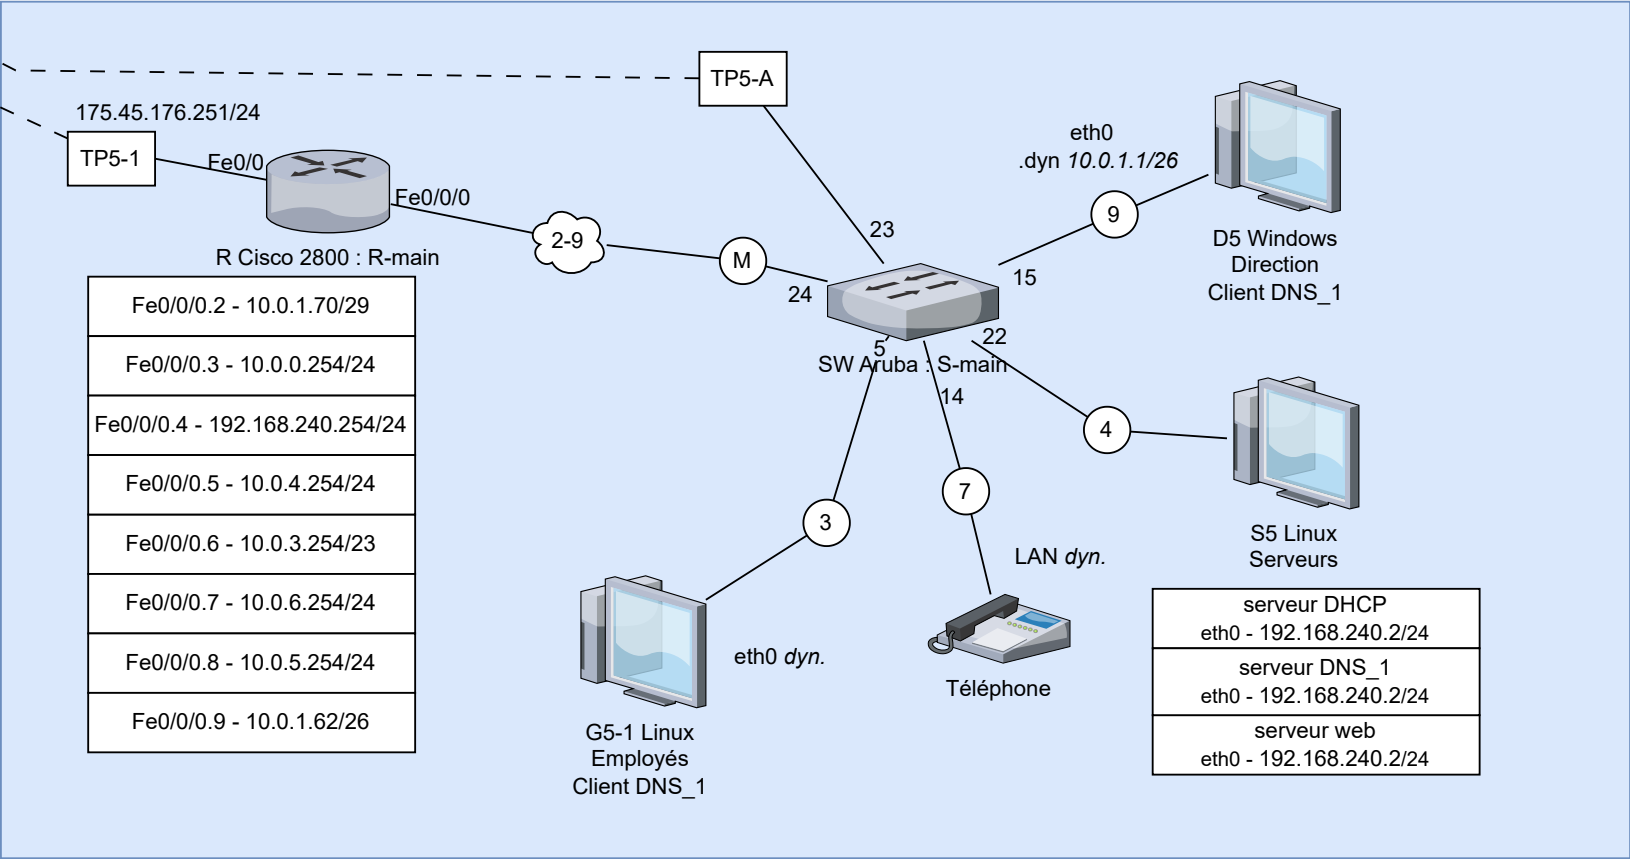

Switch (tous les switches)	
VLAN	Ports
2	2-4
3	5-7
4	22
5	8-10
6	11-13
7	14-16
8	17-19
9	20-21
liaison interswitch	23
liaison interswitch routeur	24

Légende

Icône	Signification
(M)	Lien multi-vlans
(n)	Vlan n taggé
(n)	Vlan n non taggé
TPn-A	Prise murale